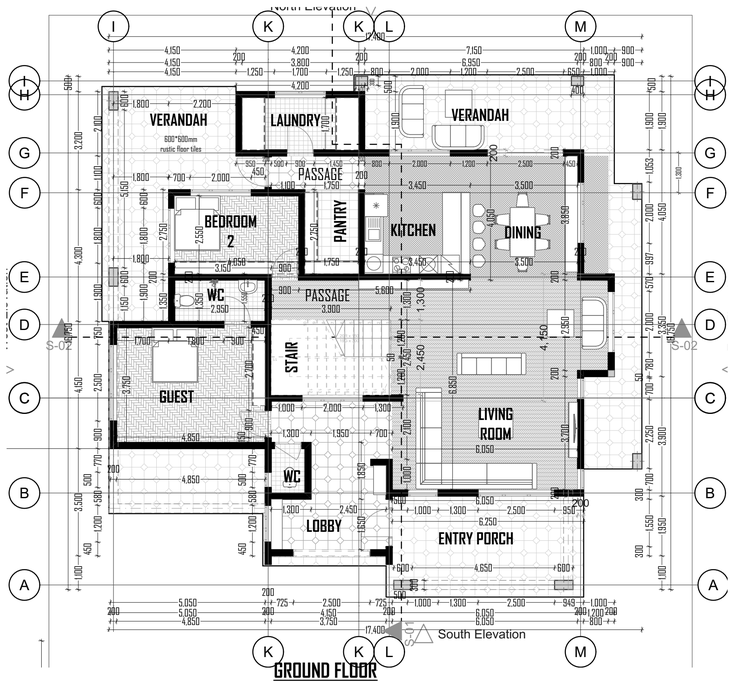

GROUND FLOOR

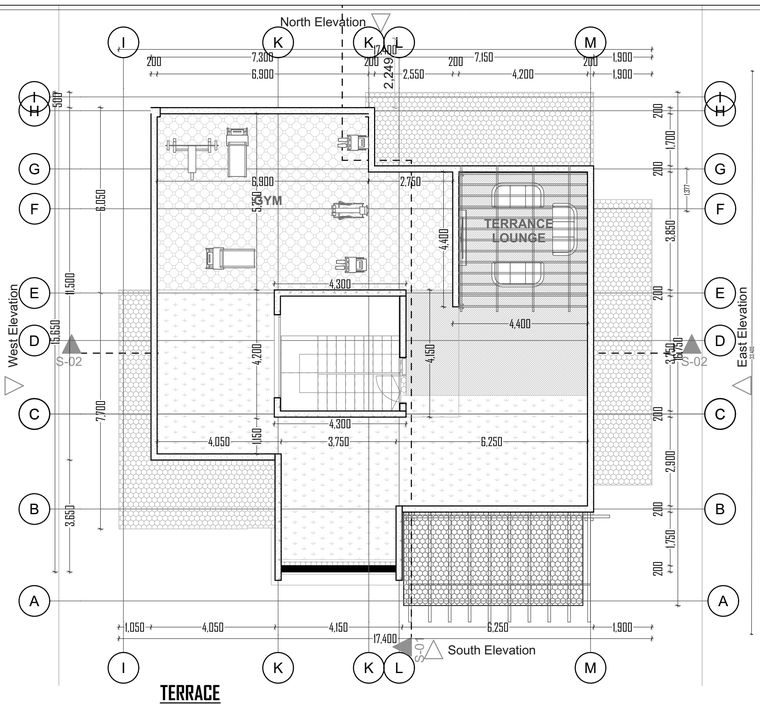

TERRACE

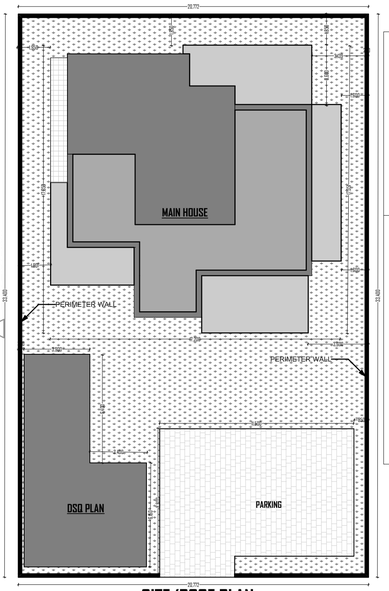

SITE/ROOF PLAN

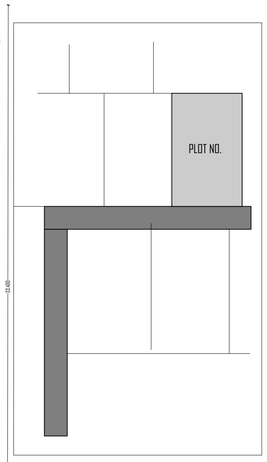

SITE LOCATION

GENERAL NOTES

1.0 Strip foundations to be 1:2:4 concrete

mix,reinforced with 3Nos.16mm dia. MS bars with 8mm dia. MS bar links at 300mm c/c,all to structural
engineer's details
.
2.0 Floor slab to be 150mm thick with wire-mesh reinforcement to structural eng's details
.
3.0 All external walls to be 200mm thick dressed bush stones and internaly with 13mm plaster and 3-
coats of emulsion paint.

40 All walls less than 200mm thick to be with hoop iron at every 4 alternative courses. All internal walls
to have 13mm plaster and 3coats of emulsion paint.

5.0 All sanitary work to be in accordance with MOH rules and regulations.

6.0 All sanitary installations to be twyfords or any other approved type to architects approval

REVISION

1. ALL THE DIMENSIONS ARE SHOWN IN MM. DRAWINGS ARE NOT TO BE SCALED. ONLY FIGURED DIMENSIONS TO BE USED.

2. THE CONTRACTOR MUST CHECK AND VERIFY ALL DIMENSIONS ON SITE BEFORE COMMENCEMENT OF WORK. ANY DISCREPANCIES MUST MUST BE NOTIFIED IMMEDIATELY TO THE ARCHITECT.

3. DAMP PROOF COURSE TO BE PROVIDED UNDER ALL EXTERNAL WALLS AT GRADE. DPC TO BE AT MINIMUM 150MM ABOVE GROUND LEVEL.

4. ALL SOILS UNDER SLABS AND AROUND EXTERNAL FOUNDATIONS TO BE POISONED FOR TERMITE CONTROL.

5. ALL WALLS LESS THAN 200MM THICK TO BE REINFORCED WITH HOOP IRON AT EVERY ALTERNATE COURSE.

6. THE FOUL AND WASTE DRAINAGE PIPES SHALL BE UPVC TO COMPLY BSS 4514. 7. DEPTH OF FOUNDATIONS TO BE DETERMINED ON SITE TO THE STRUCTURAL ENGINEER'S APPROVAL

Project:

Client: **MR CLIVE SAFARI**

Client signature: ----------

Consultants:.....

Drawn By:.. D.K.Rotich

Checked by:.....

Drawing title: plans, setions, elevations,details
SCALE 1:100

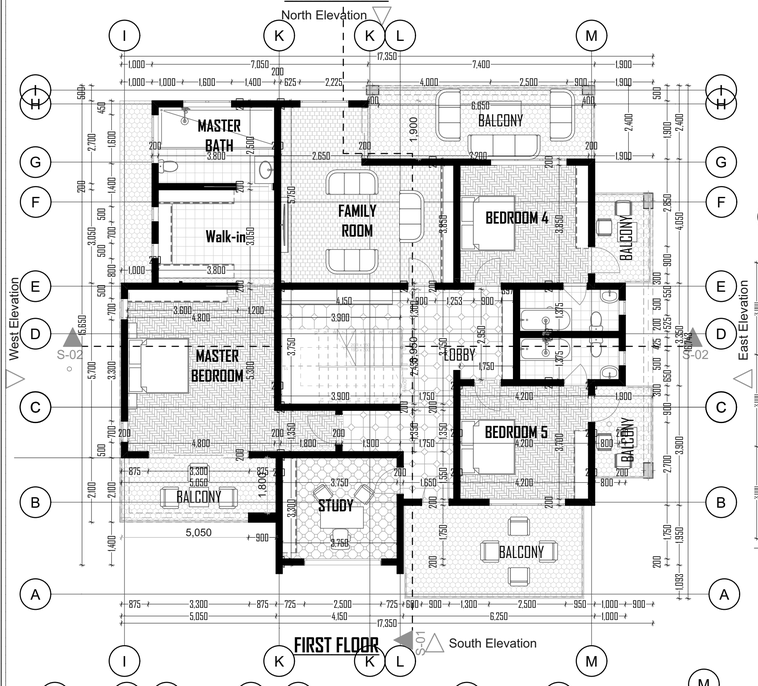

FIRST FLOOR

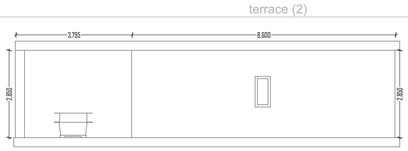

ELEVATION E-04

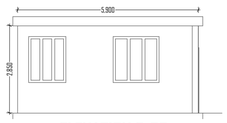

ELEVATION E-02

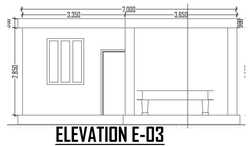

ELEVATION E-03

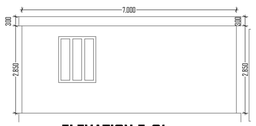

ELEVATION E-01

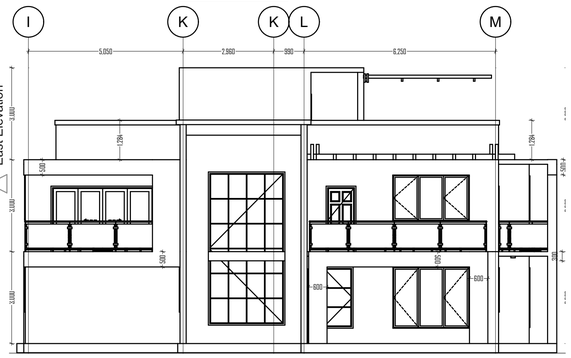

SOUTH ELEVATION

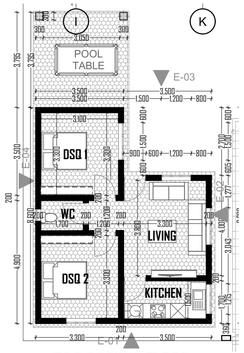

DSQ GROUND FLOOR

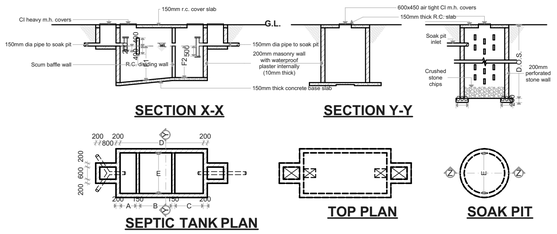

SECTION X-X

SECTION Y-Y

SEPTIC TANK PLAN

TOP PLAN

SOAK PIT

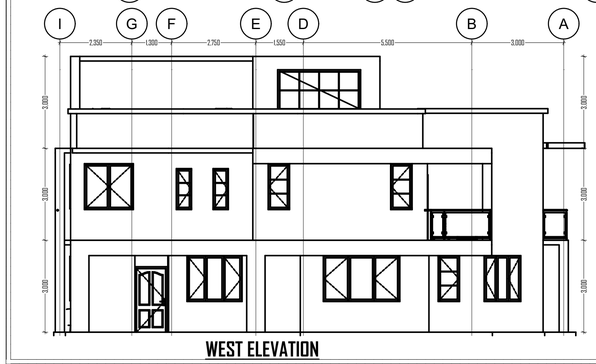

WEST ELEVATION

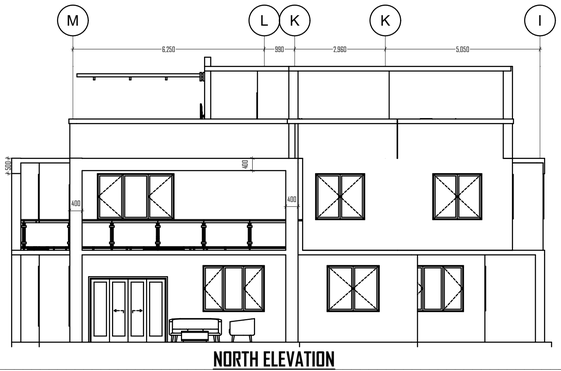

NORTH ELEVATION

EAST ELEVATION

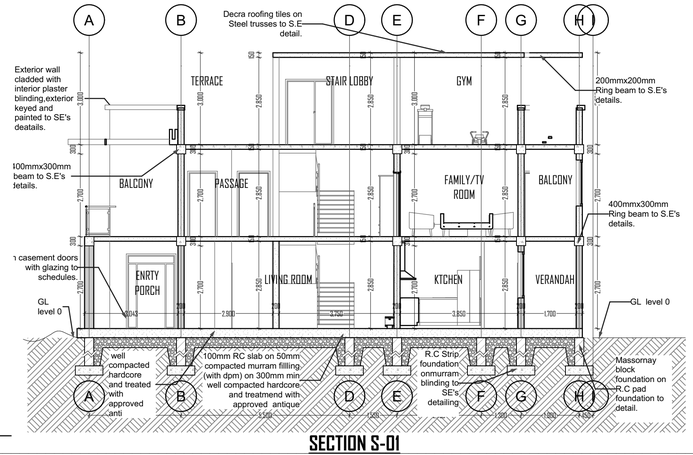

SECTION S-01